


renvooi bouwkundig

materiaal

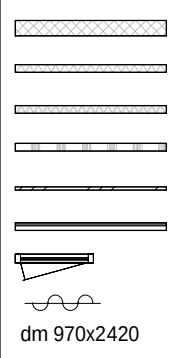

- Voorzieningen voor hemelwaterafvoer volgens opgave installatieadviseur;
- E- + W-installaties volgens opgave installatieadviseur;
- Constructies volgens tekeningen en berekeningen constructeur;
- Elektra en waterleiding conform NEN 1010 - 1006;

- Inbraakwerendheid:
Deuren, ramen kozijnen e.d. van een niet-gemeenschappelijke ruimten die volgens NEN 5087 bereikbaar zijn voor inbraak, hebben een volgens NEN 5096 bepaalde inbraakwerendheid die voldoet aan de in die norm aangegeven weerstandsklasse 2 conform afd. 2.15 Bouwbesluit; tot een hoogte van 5.5 m1 dient de gevel te voldoen aan weerstandsklasse 3

- Bescherming tegen ratten en muizen:
Openingen uitwendige scheidingconstructie max. 0.01 m. breed
Een uitwendige scheidingconstructie, heeft een scherm tot een vanaf het aansluitende terrein gemeten diepte van ten minste 0.6m en openingen max. 0.01 m. breed
conf. afd. 3.10 Bouwbesluit;

- Wering van vocht van buiten:
In- en uitwendige scheidingconstructies verblijfsgebied, toiletruimte of badruimte waterdicht volgens bepaling NEN 2778. Luchtvolumestroom scheidingconstructie verblijfsgebied, toiletruimte of badruimte en kruipruimte max. 20*10 -6 m3/(m²*s), volgens bepaling NEN 2690 conform afd. 3.5 Bouwbesluit;

- Wering van vocht van binnen:
Wateropname scheidingconstructies toilet- en badruimten tot 1.2 m. max. 0.01 kg/(m² * s^{1/3}), behoudens t.p.v. bad- en douche tot 2.1 m. met min. lengte van 3 m. Vanaf 1.2 m. max 0.2 kg/(m² * s^{1/3}) volgens bepaling NEN 2778 conform afd. 3.5 Bouwbesluit;

- Toegankelijkheidssector:
Max. hoogteverschil vloer t.p.v. van toegang toegankelijkheidssector en aansluitende terrein en vloeren in toegankelijkheidssector 0.02 m. conform afd. 4.4 Bouwbesluit;

renvooi aspectmodellen

Eigenaar	Naam aspectmodel	Datum
		18-01-2024
		27-01-2024
		27-01-2024

renvooi brandveiligheid

- Ra weerstand tegen rookdoorgang tussen 2 ruimten
- weerstand tegen branddoor- en brandoverslag (wbdb) > 60 minuten
- weerstand tegen branddoor- en brandoverslag (wbdb) > 90 minuten
- weerstand tegen branddoor- en brandoverslag (wbdb) > 120 minuten
- weerstand tegen branddoor- en brandoverslag (wbdb) > 180 minuten

- zelfsluitende deur met een rookwerendheid Sa vlgs de NEN-EN 1634-3.
- zelfsluitende deur met een WBDBO >= 30 minuten
- zelfsluitende deur met een WBDBO >= 90 minuten
- zelfsluitende deur met een WBDBO >= 120 minuten
- ruimte voorzien van noodverlichting
- brandslanghepel volgens NEN 671-1 in omkasting, in/op wand
hart 1 trommel tussen 1.0-1.5m +/-p, lengte 30 meter
- handblusser, 6KG CO2
- brandweerpaneel vlgs. NEN 2535
- voedingaansluiting droge busleiding
- brandslangaansluiting droge busleiding
- brandhydrant
- vluchtrouteverlichting elektrisch
- nooddeur 1100x2400
opschrift "nooddeur vrijhouden" of "nooddeur"vlgs. NEN 3011

dagmaten vluchturen minimaal 850 x 2300

- Gebouw te voorzien van brandmeldinstallatie:

De brandmeldinstallatie wordt uitgevoerd vlgs. NEN 2535. Omvang van de bewaking: volledig. De brandmeldinstallatie heeft een rechte reeks doormelding naar de meldkamer

Programma van eisen wordt opgesteld en ter goedkeuring aangeboden aan het bevoegde gezag.

- Gebouw voorzien van ontruimingsinstallatie:

en het gebouwgebonden UPD van gebouw 10AC. Programma van eisen wordt opgesteld en ter goedkeuring aangeboden aan het bevoegde gezag.

- Gebouw voorzien van sprinklerinstallatie:

gebouwgebonden UPD van gebouw 10AC. Programma van eisen wordt opgesteld en ter goedkeuring aangeboden aan het bevoegde gezag

- Bouwconstructie bij brand:

De bouwconstructie bij brand wordt 60 minuten brandverend uitgevoerd vlgs. BB. art. 2.10

- Beperking ontwikkeling van brand en rook:

Buitenoppervlak:
Materialen voldoen aan brandklasse A vlgs. NEN-EN 13501-1, BB art. 2.6

De bovenzijde van vloer-, trap- en hellingbaanconstructie voldoen aan brandklasse Af vlgs. NEN-EN 13501-1, BB art. 2.69


- Binnenoppervlak
Materialen voldoen aan brandklasse A vlgs. NEN-EN 13501-1, BB art. 2.6

De bovenzijde van vloer-, trap- en hellingbaanconstructie voldoen aan brandklasse Af vlgs. NEN-EN 13501-1, BB art. 2.69

- Een vluchtroute leidt naar een veilige plaats zonder dat gebruik behoeft te worden gemaakt van een lift. Deuren in deze vluchtroute zijn uitsluitend gesloten indien die deur tijdens het vluchten, zonder gebruik te moeten maken van een sleutel onmiddellijk over de tenminste vereiste breedte kan worden geopend. vlgs BB. art. 7.12

- Een besloten ruimte waardoor een beschermde vluchtroute voert, heeft een verlichtingsinstallatie die een op de vloer en het tredevlak gemeten verlichtingssterkte kan geven van ten minste 1 lux, vlgs. BB. art. 6.2

- Een verlichtingsinstallatie aangesloten op een voorziening van noodstroom geeft binnen 15 sec. na het uitvalven van de voorziening voor elektriciteit, gedurende ten minste 60 minuten een op de vloer en het tredevlak gemeten verlichtingssterkte van ten minste 1 lux, vlgs. BB. art. 6.3

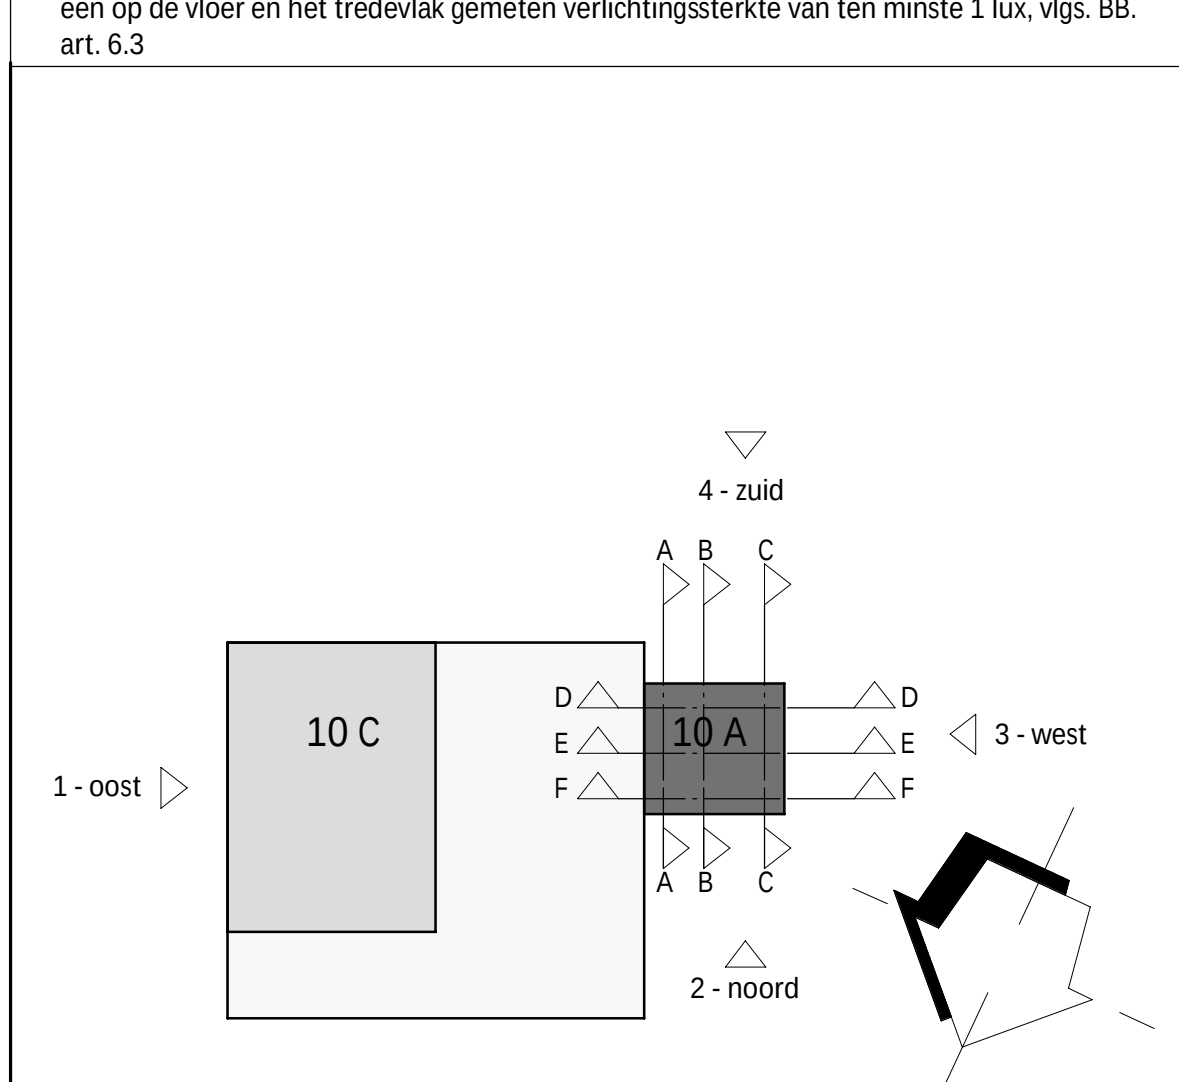

Peil = 21.000 mm + NAP

A	02-02-2024	BMW	NSA-ruimtes en gevel op HOLD
wijziging	datum	getek	omschrijving

A	02-02-2024	BMW	NSA-ruimtes en gevel op HOLD
wijziging	datum	getek	omschrijving

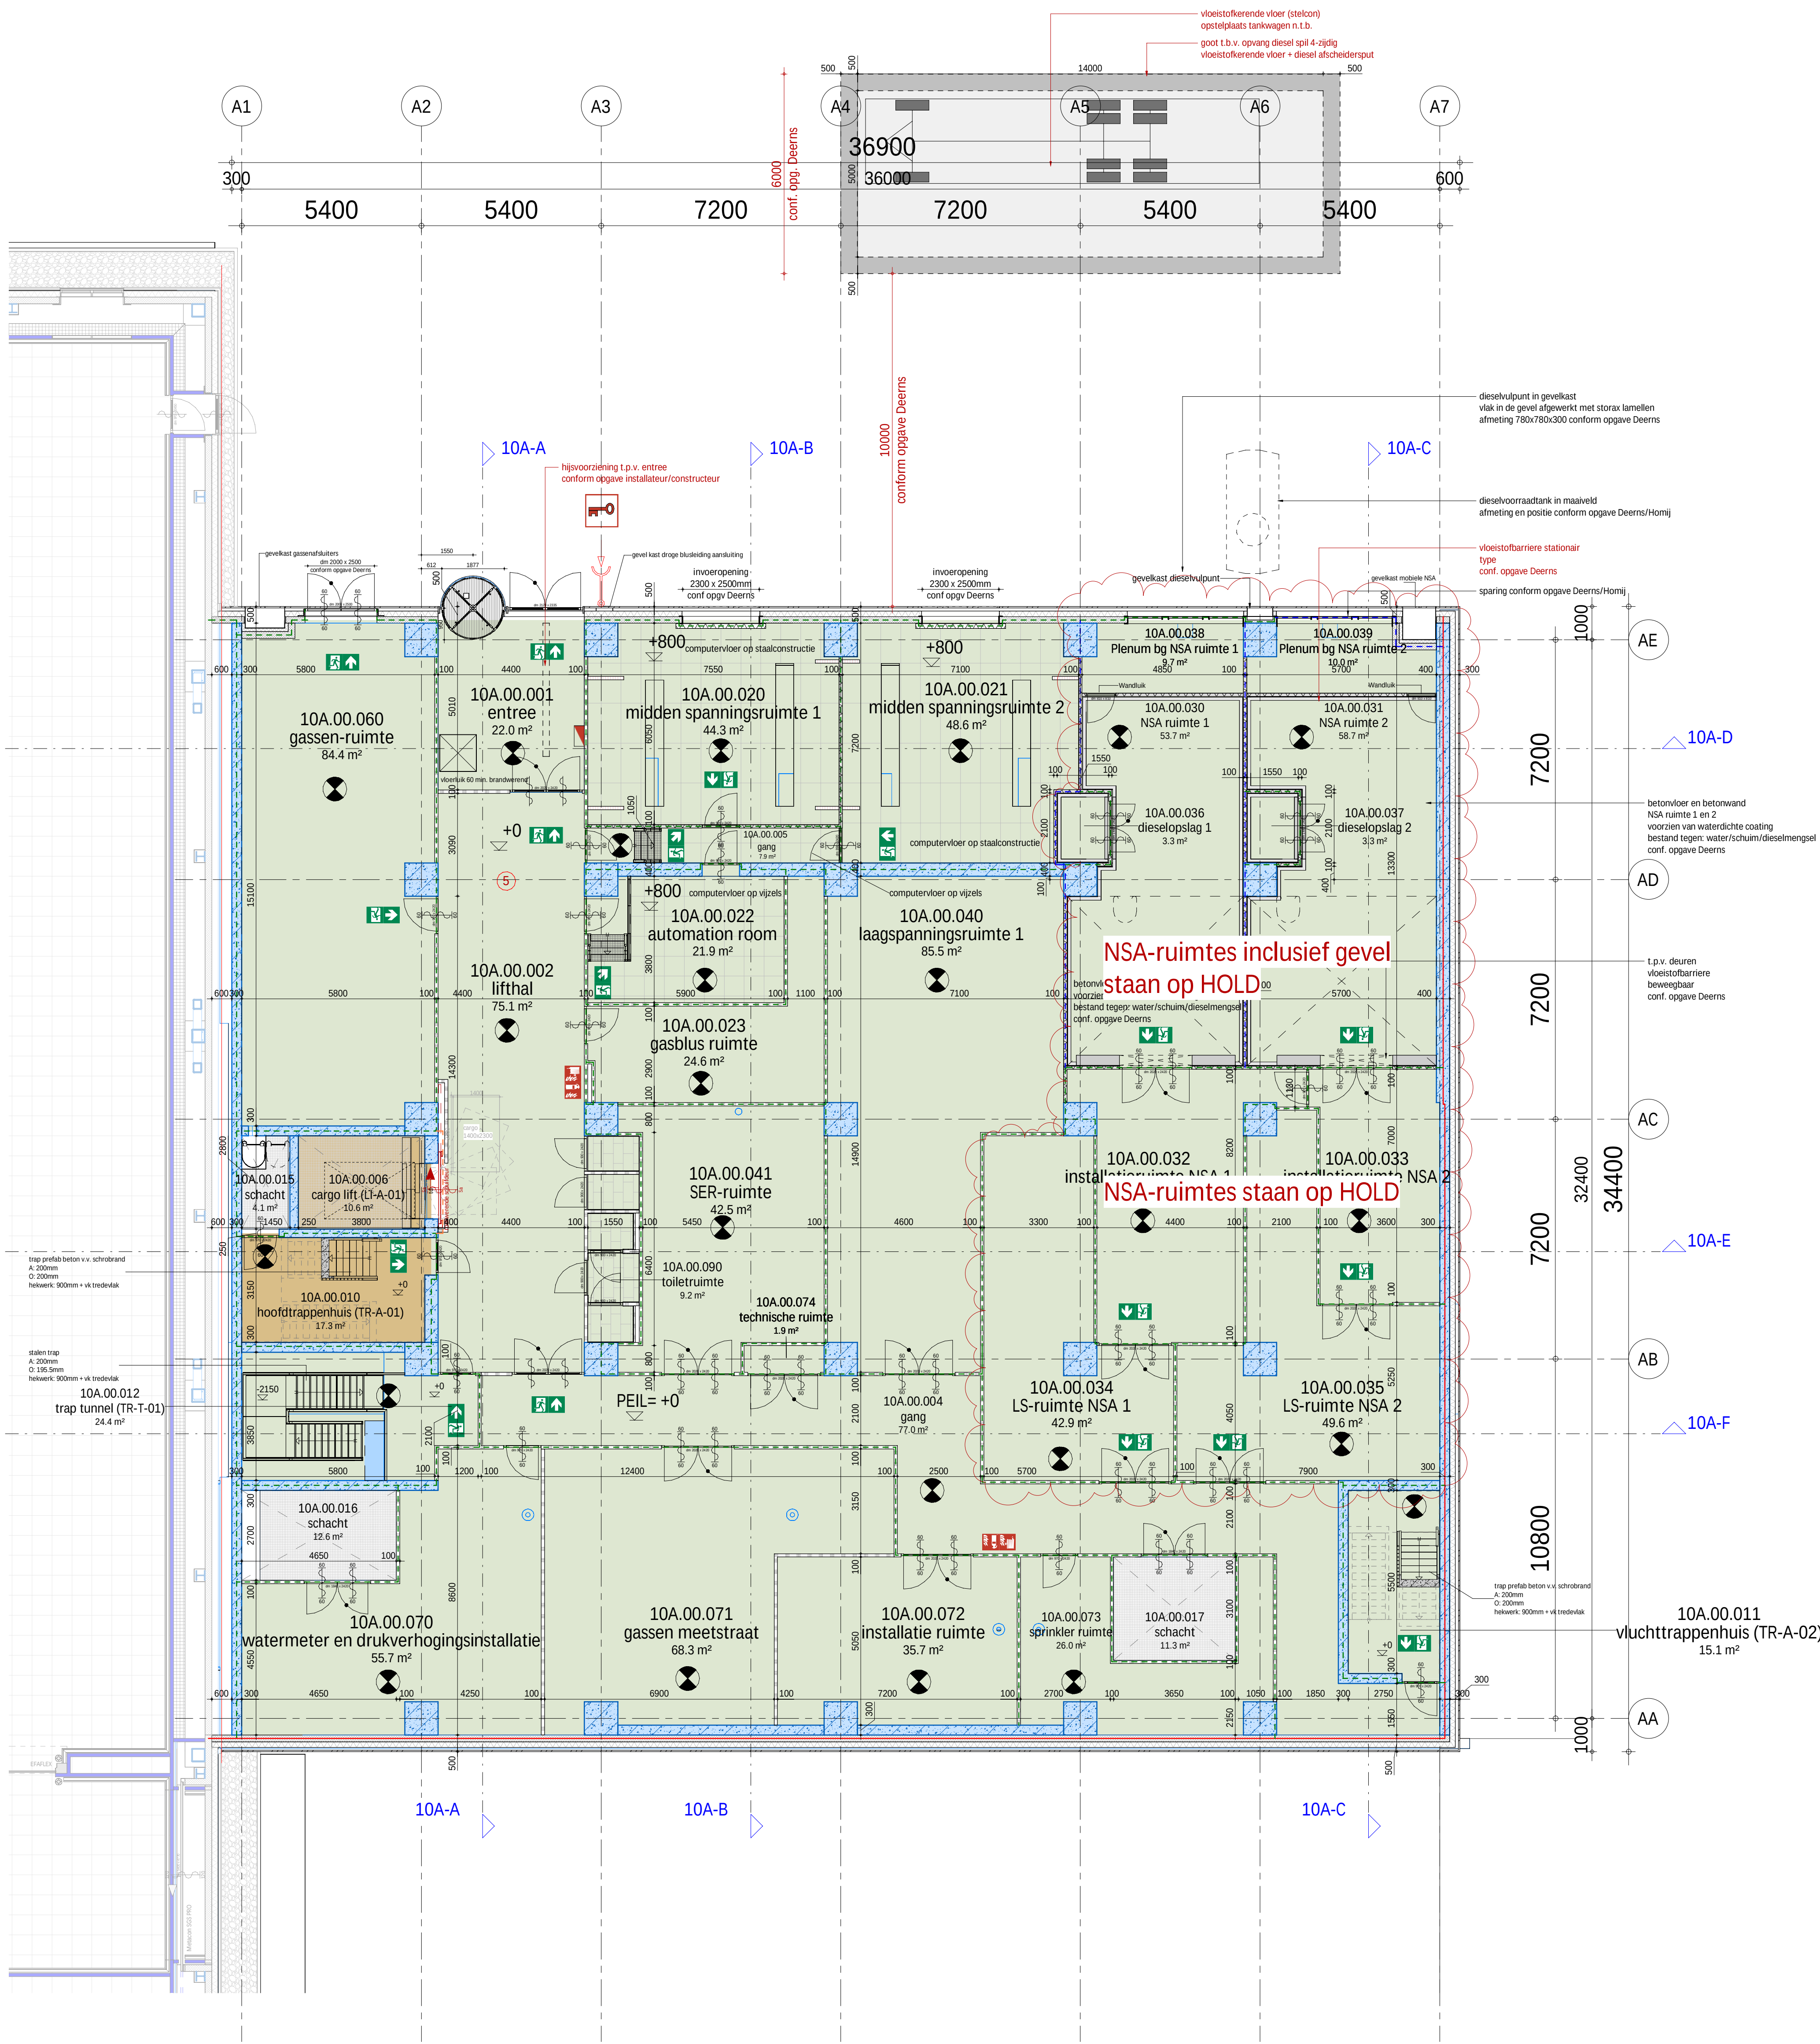

begane grond

VAN AKEN Part of Sweco			
IN BEWERKING 02-02-2024			
plattegrond begane grond 10			
22008	datum	-	
	status	voorlopig	
	schaal	1:100	
	formaat	A0	