


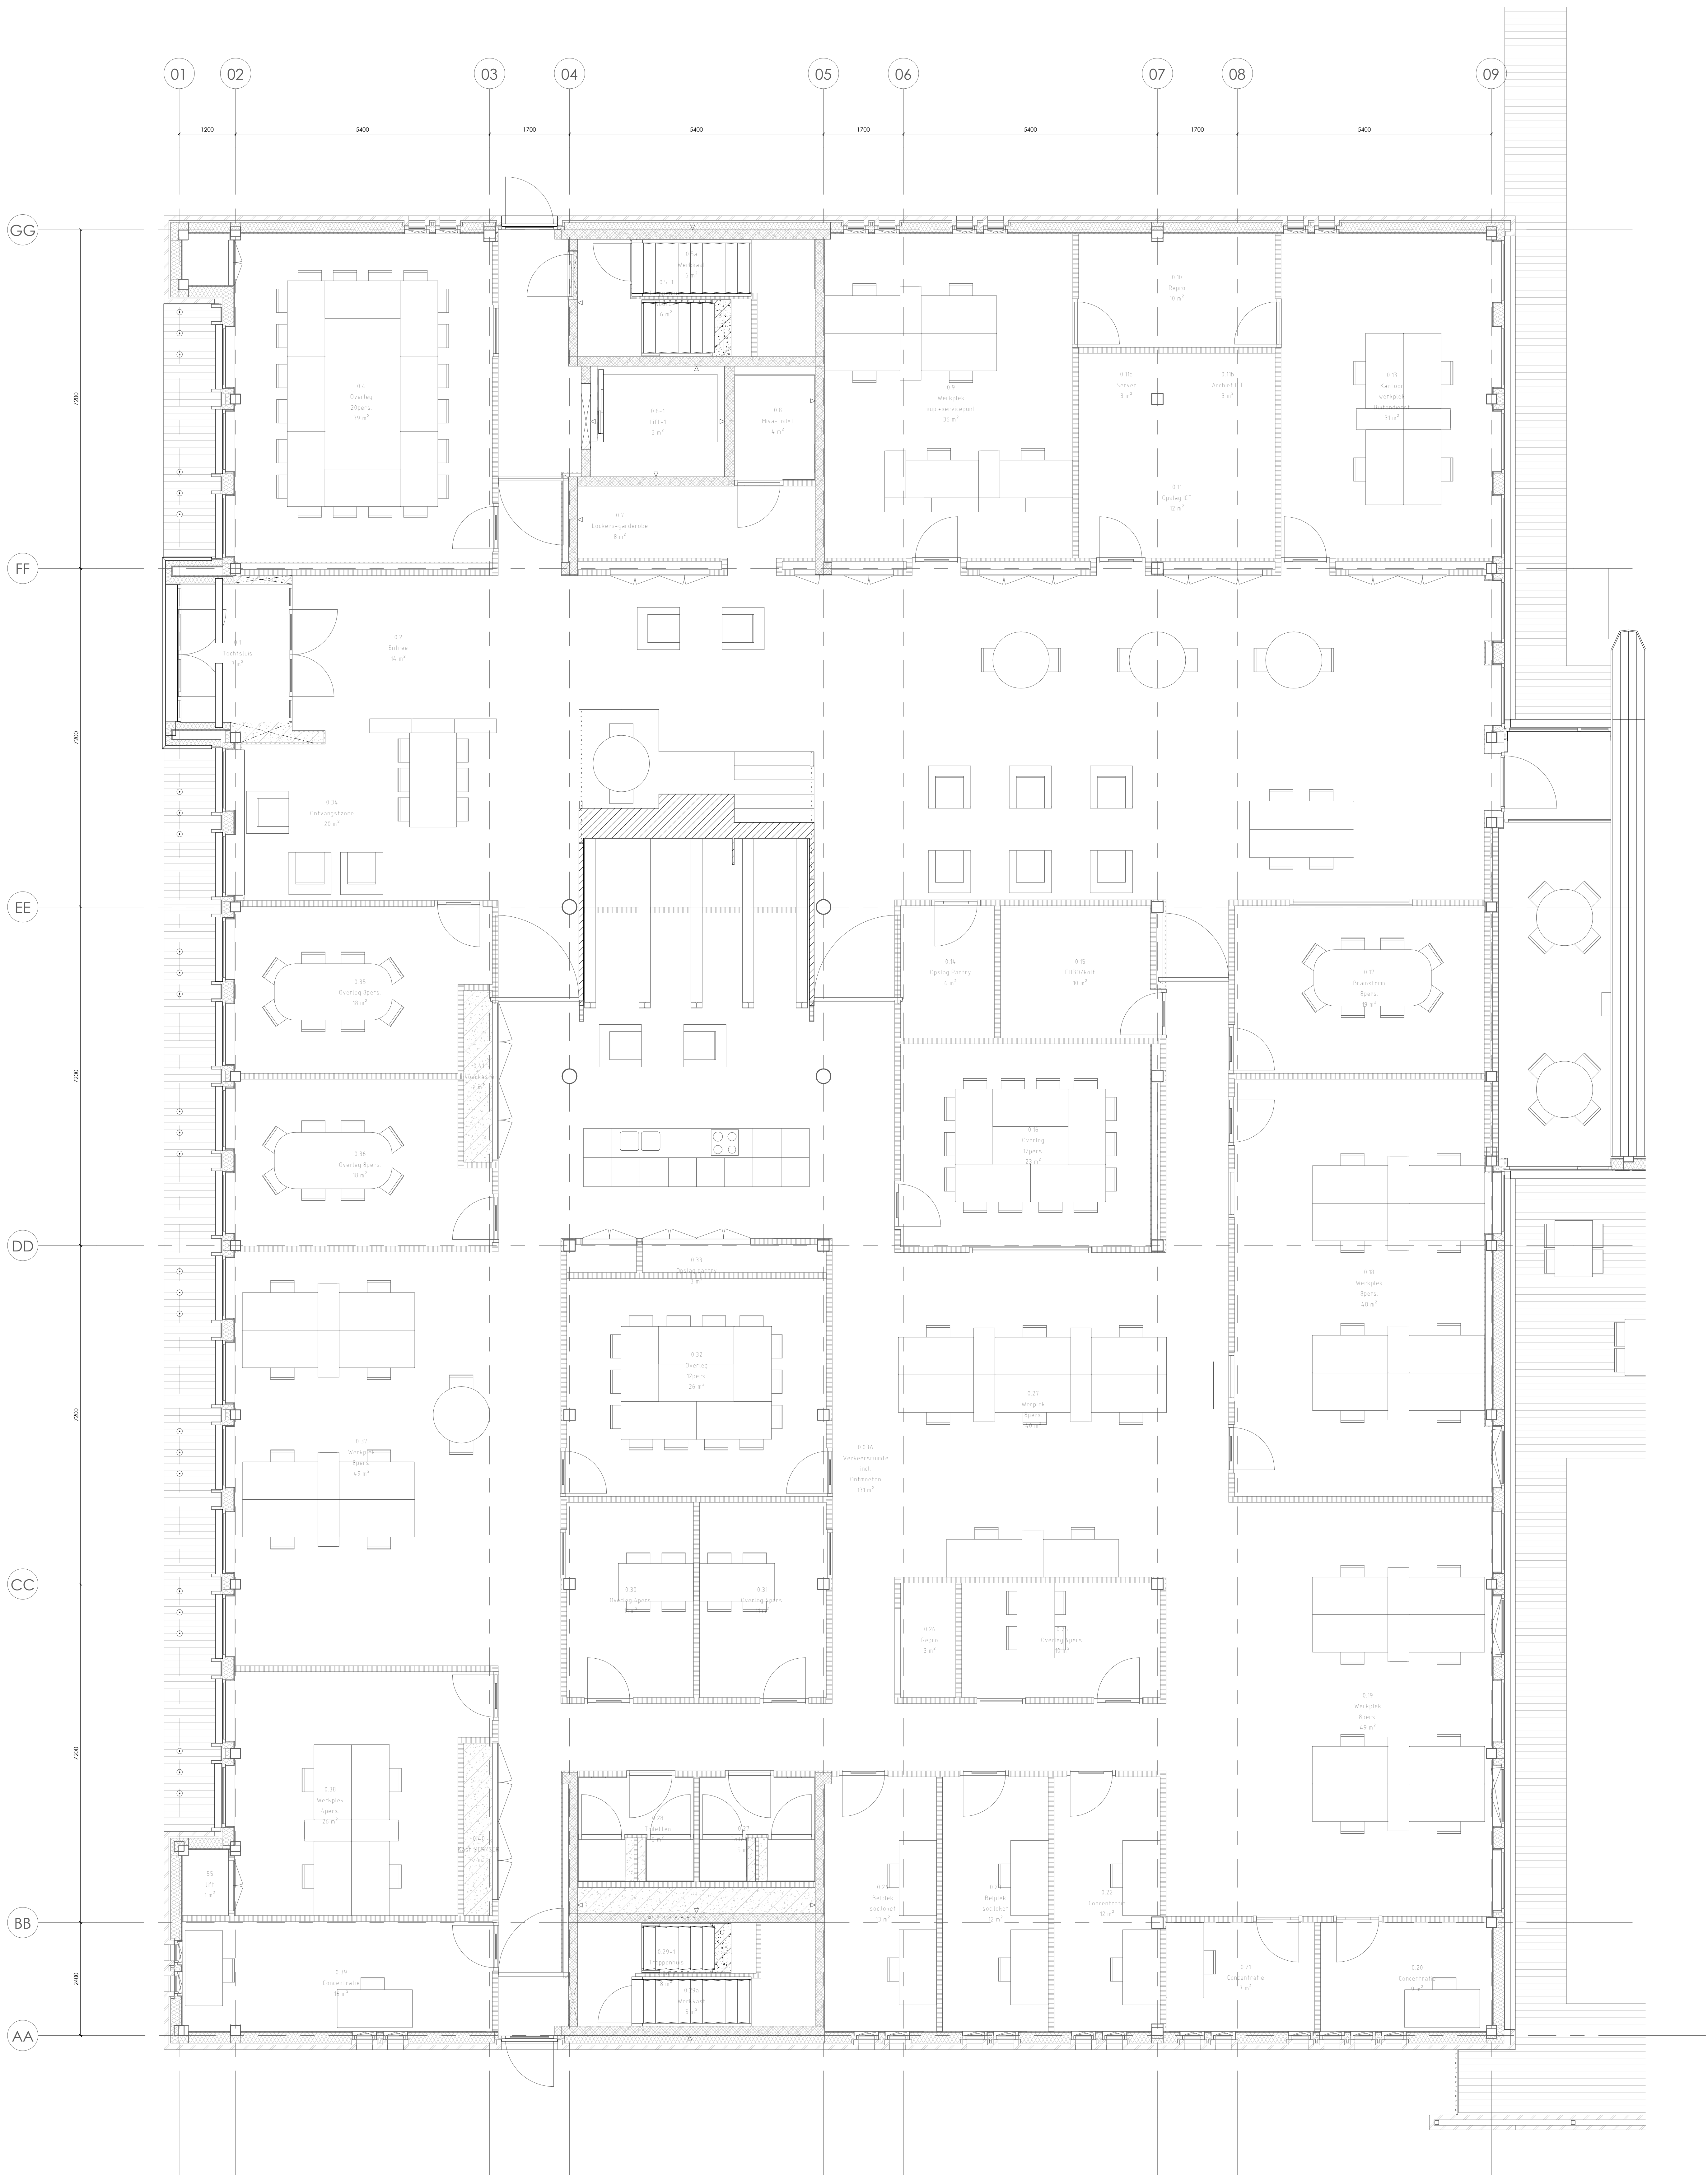

project Nieuwbouw werklocatie Molenlanden
kenmerk 2038
onderwerp Begane grond - Kantoor
installatie CV, GW en Luchtbehandelings installaties

opdrachtgever Gemeente Molenlanden
architect DAT architecten te Tilburg

blad W-0a
fase Bestek
status Definitief
schaal 1:50
formaat A0
datum arch 01-02-2022
datum 01-02-2022
gewijzigd



www.lin.nl
info@lin.nl
+31 (0)20 5507878

entrepotdok 81
1018 ad
amsterdam